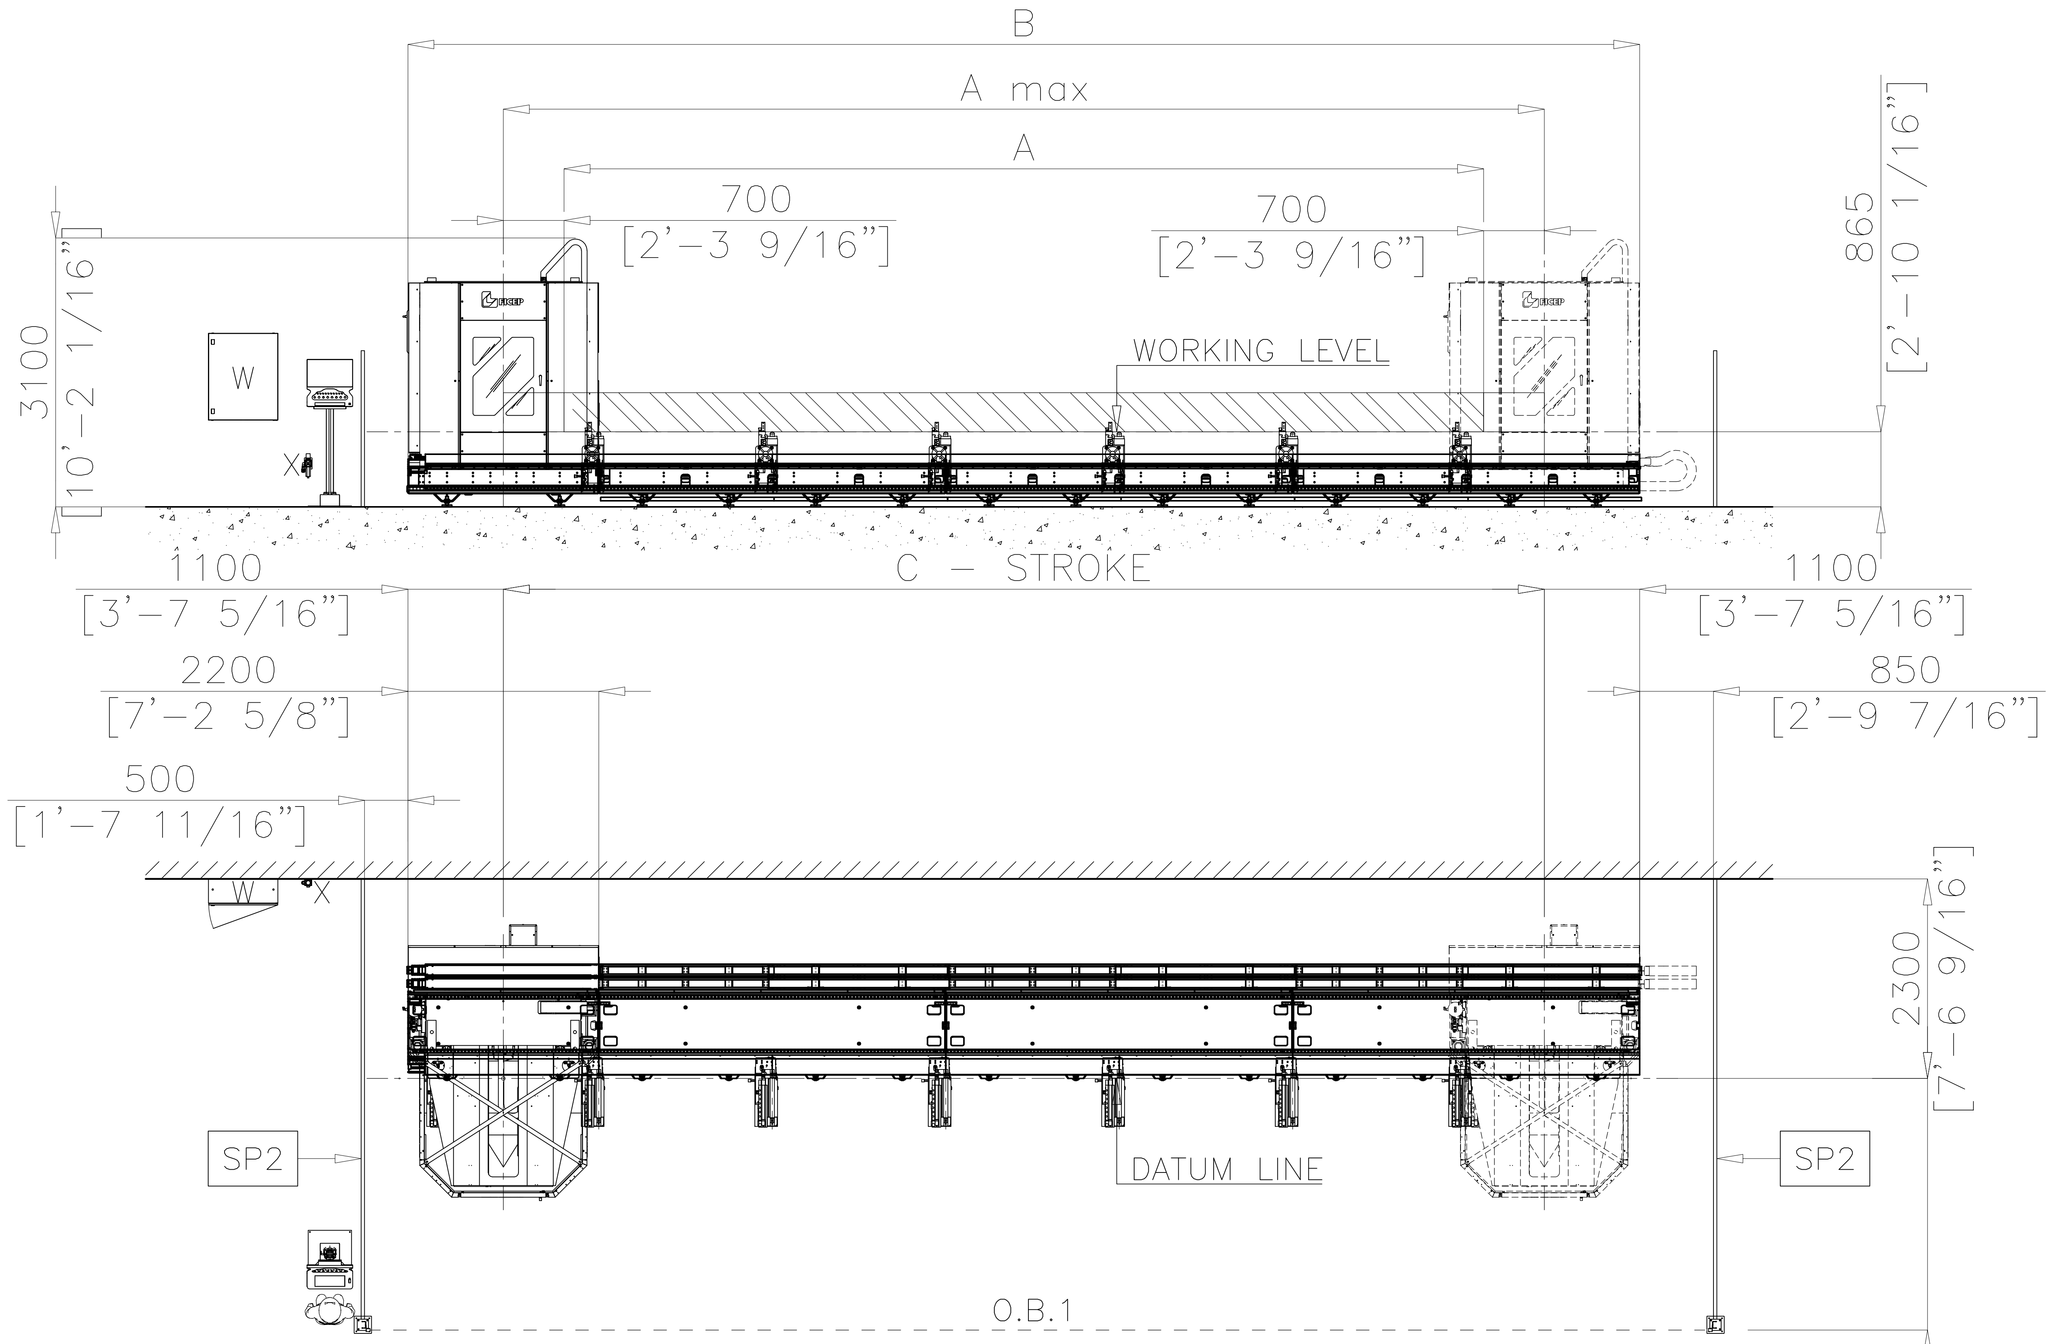

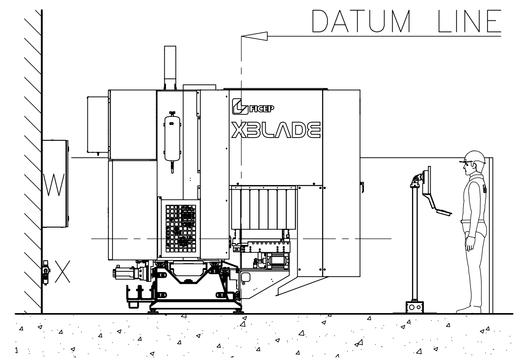

SECTION NOMINAL LENGTH	12m	16m	20m	24m	28m
A (Max)	12000	16000	20000	24000	28000
B	14200	18200	22200	26200	30200
C	12000	16000	20000	24000	28000
nr. vices (standard)	6	6	12	12	12

O.B./G.T.	STOP
O.B.1	ALL

Protecting barrier to meet safety standards requirements in force for the construction, and positioned to prevent the admittance of any person into the machine area.
The wire net protection must be of the metal type with supporting tubes secured to the floor by bolts (refer to note A).
The final configuration to be checked and approved by the local anti-hazard inspectors.

ALTEZZA DI LAVORO 865mm
WORKING LEVEL 865mm
WORKING LEVEL 2' 10'' 1/16

nota A

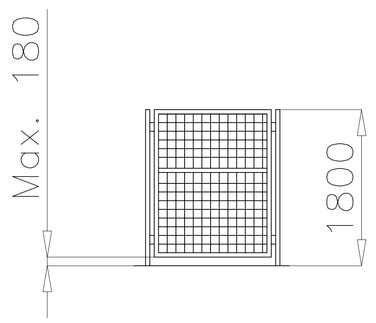

Fixed guards must have the following features:

> Metal wire mesh guards, 32x67 wire ø3 or 40x40 wire ø3 - ø4
> Max. distance from the ground: 180 mm
> Min. total height: 1800 mm

O.B. = Light barrier that stops system movements. Barrier reset only possible using the push-button panel on the control console located outside the safety fence.

W - TOTAL INSTALLED POWER 38kW 400V 3Ph. 50Hz
X - AIR CONNECTION 1/2" GAS - MIN. AIR 20Nm^3/hour 6bar

REV.	DATA	DESCRIZIONE	FIRMA
4	../../..	---------	.....
3	../../..	---------	.....
2	../../..	---------	.....
1	../../..	---------	.....
0	10/04/25	FIRST LAYOUT	Bossi A.

CAD DRAWING

LAYOUT XBLADE

MACCHINA 301XB5
MOD. - GRAND. -

DISEGNO N. DES66677 | AGGIORNAM. . - | TAVOLA 1. -

SCALA	DISEGNATO	DATA
1:100	Bossi A.	10/04/25
SOST. IL DIS.	Bossi A.	10/04/25
SOST. DAL DIS.	Fongaro S.	10/04/25

FICEP S.p.A.
Gazzada Schianno 21045 - VARESE (ITALY)
TELEFONO (0332) - 876111
TELEFAX (0332) - 462459
EMAIL ficep@ficep.it

AVVERTENZA! QUESTO DISEGNO E' DI NS. PROPRIETA'; PERTANTO CHI LO UTILIZZASSE A PROPRIO O ALTRUI PROFITTO E' PERSEGUIBILE A TERMINE DI LEGGE.